① 현황 평면도 (실측) / 現況平面図（実測）

축척 1:50 (A3 원본 인쇄 시). 치수 단위 m. 숫자가 그림보다 우선. 벽 번호 W, 기둥 번호 C 는 3D 뷰어와 같음.

✓ 실측 2026-11-07 / 実測 · (스캔) = 3D 스캔 추정 / スキャン推定 — 着工前に現場再確認

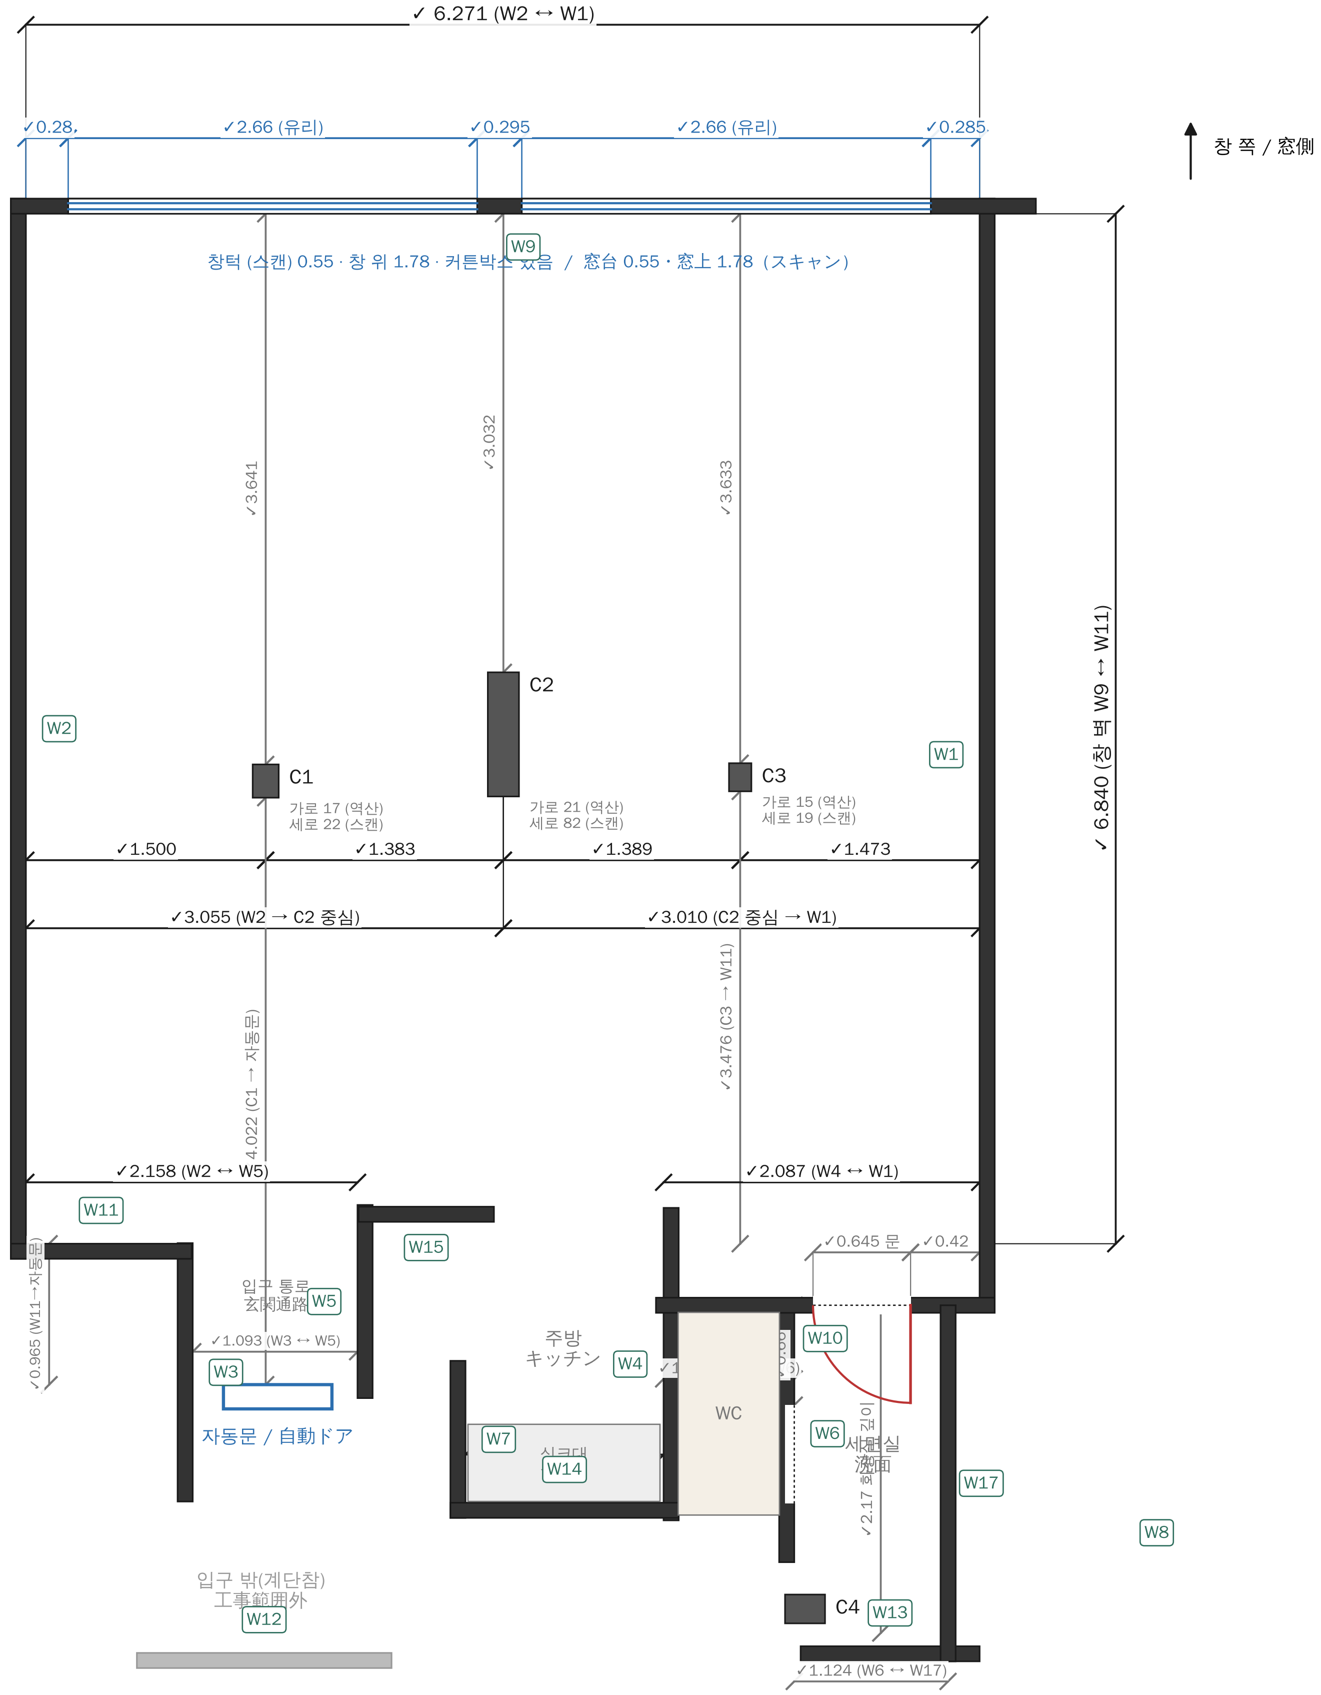

높이 실측 / 高さ実測

천장고 / 天井高	✓ 2.393 m
검은 띠(체어레일) 높이 / 黒い帯	✓ 7.4 cm · 벽에서 1.0 cm 돌출
바닥→띠 위끝 / 床→帯上端	(스캔) 약 0.89 m — 미실측
바닥→띠 아래끝	(스캔) 약 0.81 m — 미실측
걸레받이(나무) / 幅木	✓ 11.2 cm · 돌출 0.4~0.7 cm
창턱 높이 / 窓台	(스캔) 0.55 m
바닥 / 床	원목 마루 — 그대로 둠 / 既存のまま
벽지 / 壁紙	회색 비닐 벽지(추정) — 상태 확인 필요

미실측·확인 필요 / 要現場確認

- 바닥→검은 띠 위끝 높이 (판 길이 900 결정)
- 기둥 C1~C3 가로·세로 직접 측정 (가로는 역산값)
- 창 폭 2.66 이 유리인지 틀 포함인지 (합계 6.18 vs 방 폭 6.271)
- 자동문 폭, W11·W3 길이, 콘센트·스위치 위치
- 벽지 종류(비닐/오염방지 코팅) — 페인트 밀착 확인
- 벽 5·15 근처 1.77 m · 0.8 m 메모 구간

범례 / 凡例

■ 기존 벽 / 既存壁
▨ 공사 범위 밖 / 範囲外
□ 창 / 窓
■ 기둥 C / 柱

② 계획 평면도 — E안 / 計画平面図（E案）

신설 벽·막음·개구부·바닥 마감·고정 가구 위치. 치수 단위 m. 소품(의자·세트)은 배치 참고.

✓ 실측 2026-11-07 / 実測 · (스캔) = 3D 스캔 추정 / スキャン推定 — 着工前に現場再確認

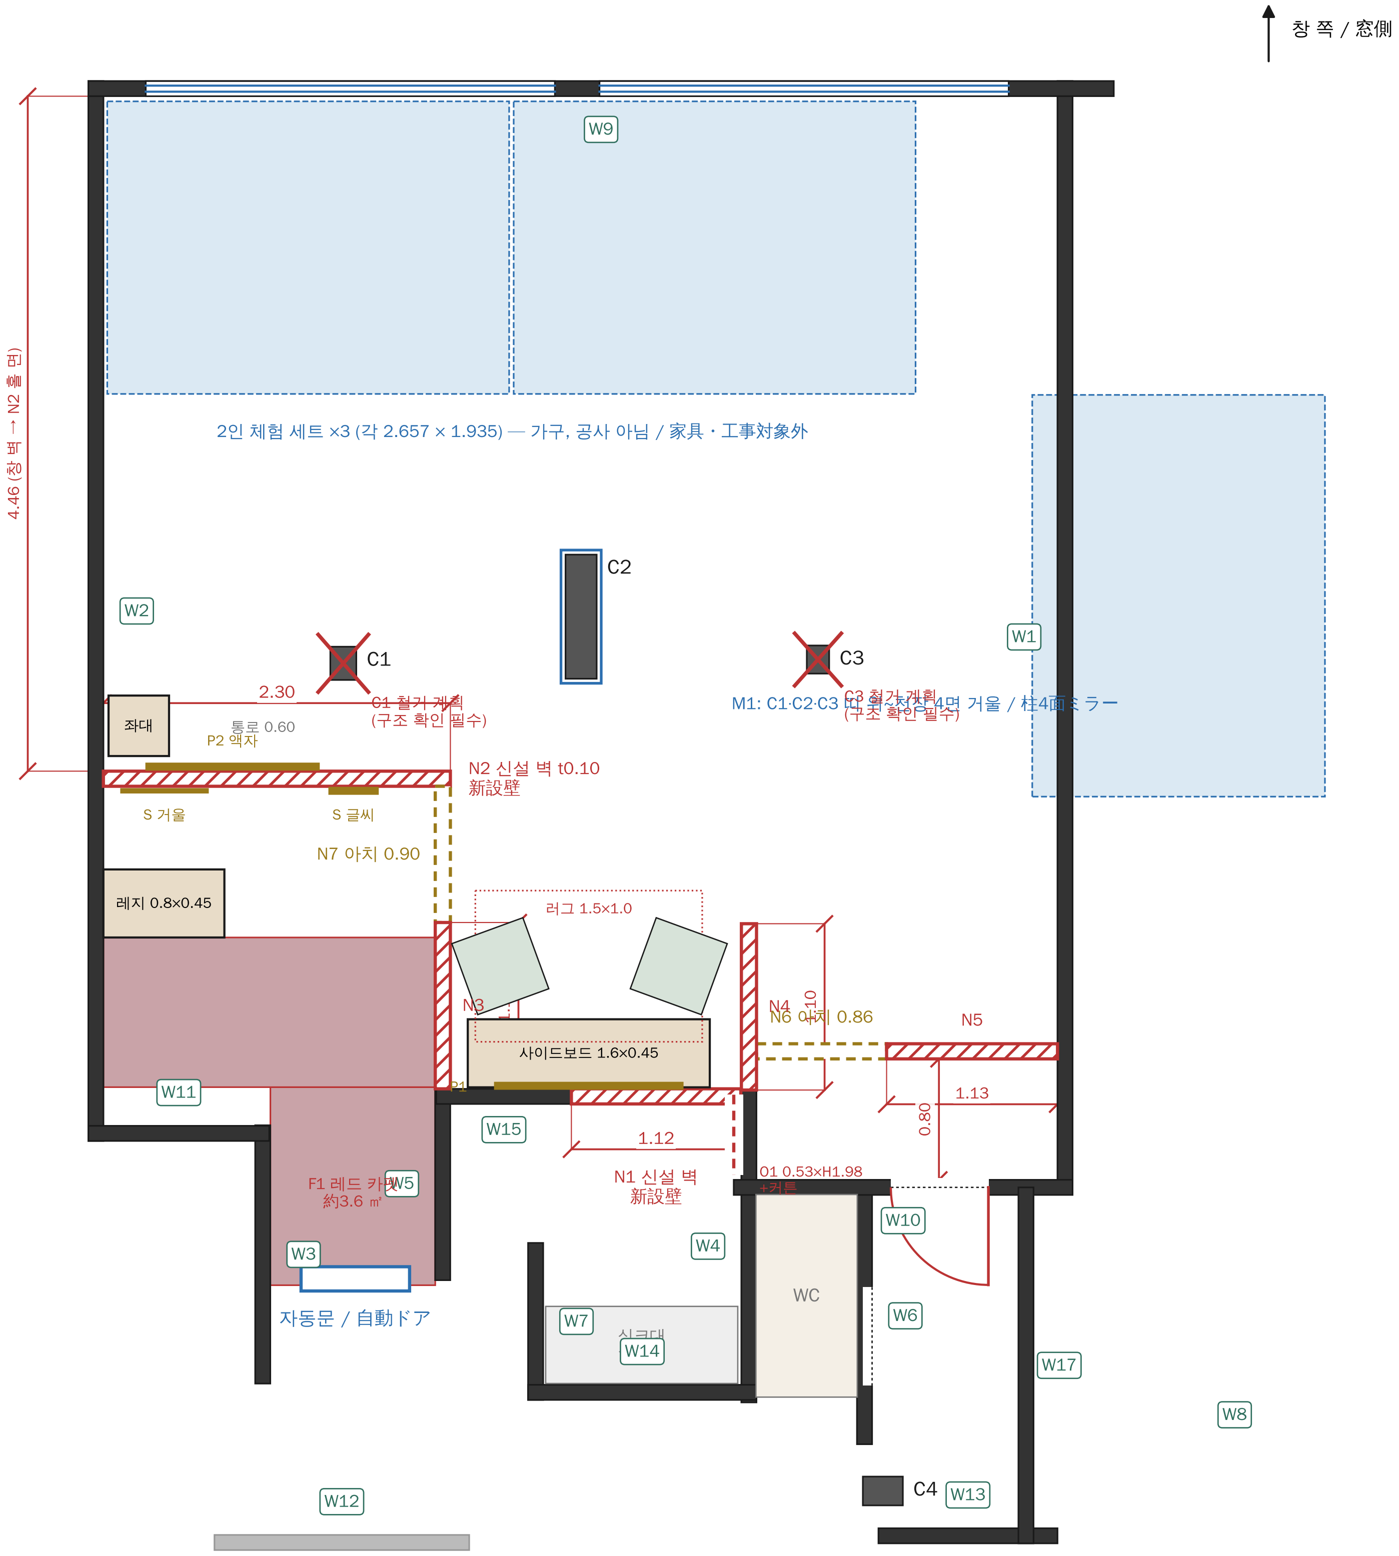

공사 항목 / 工事項目

N1	주방 입구 막음 벽 1.12 × H2.39, t0.10 — LGS/목틀 + 석고보드, 양면 홀 마감
N2	레지 뒤 벽 2.30 × H2.39, t0.10 — 남면 크림슨 페인트(#8A1F2B), 북면 홀 마감
N3·N4	사진 코너 양쪽 날개벽 각 1.10 × H2.39, t0.10 — W15 북면·W4 북쪽 끝에서 홀 쪽으로, 홀 마감
N5	화장실 문 가림벽 1.13 × H2.39, t0.10 — 문 벽에서 0.80 평행, 동쪽 끝 W1 에 붙임
N6	세면실 아치 출입구 0.86 × 2.05(반원, 스프링 1.62) — N4~N5 사이, 상부 스팬드럴 + 금색 몰딩
N7	홀 입구 아치 0.90 × 2.07(반원, 스프링 1.62) — N2 동쪽 끝 ~ N3 사이, 상부 스팬드럴 + 금색 몰딩
D	C1·C3 철거 계획 — 구조 기둥 여부 확인 후 결정
P3	화장실 문 앞 포토 스폿 — 문 앞 0.8 m 공간 네 면 리프 모자이크 타일(베이지) + N5 안쪽 면 금테 타원 거울 64×92 + 스포트 1
D2	화장실 문 교체 — 경첩 동쪽(W1 쪽)·세면실 안쪽으로 여는 문
O1	W4 에 개구 0.53 × H1.98 (직원 통로) + 검은 봉·암막 커튼
F1	레드 카펫 약 3.6 ㎡ (입구 통로 + 레지 앞), 기존 마루 위
P1	사이드보드 코너(W15·N1 앞): 벽 거울 1.2×0.6 걸이, 사이드보드 1.6×0.45 반입
P2	N2 북면: 액자 1.1×0.85 걸이, 좌대
M1	기둥 C1·C2·C3 띠 위~천장 4면 거울 (비산방지 필름)
S	N2 남면: 船場美術館 세로 금박 절단문자 H1.1(통로 정중앙) + 원형 거울 φ0.55(레지 위)
L	트랙 스포트라이트 3 등 추가 (사이드보드 2 · P2 1)

범례 / 凡例

- ▨ 신설 벽 / 新設壁
- 🟥 레드 카펫 / 赤カーペット
- ⬚ 체험 세트 영역(가구)
- ▭ 고정 가구 위치(반입)

※ 벽·바닥·천장 마감은 ③ 참조. 임대 원상복구 조건 확인 후 고정 방식 결정.

③ 벽 마감 상세 / 壁仕上げ詳細

전 벽 공통 단면 (큰방 W1·W2·W9·W10·W15·W18·N1·N2 홀 면·기둥). 단위 mm. 높이 A 는 현장 실측 후 확정.

✓ 실측 2026-11-07 / 実測 · (스캔) = 3D 스캔 추정 / スキャン推定 — 着工前に現場再確認

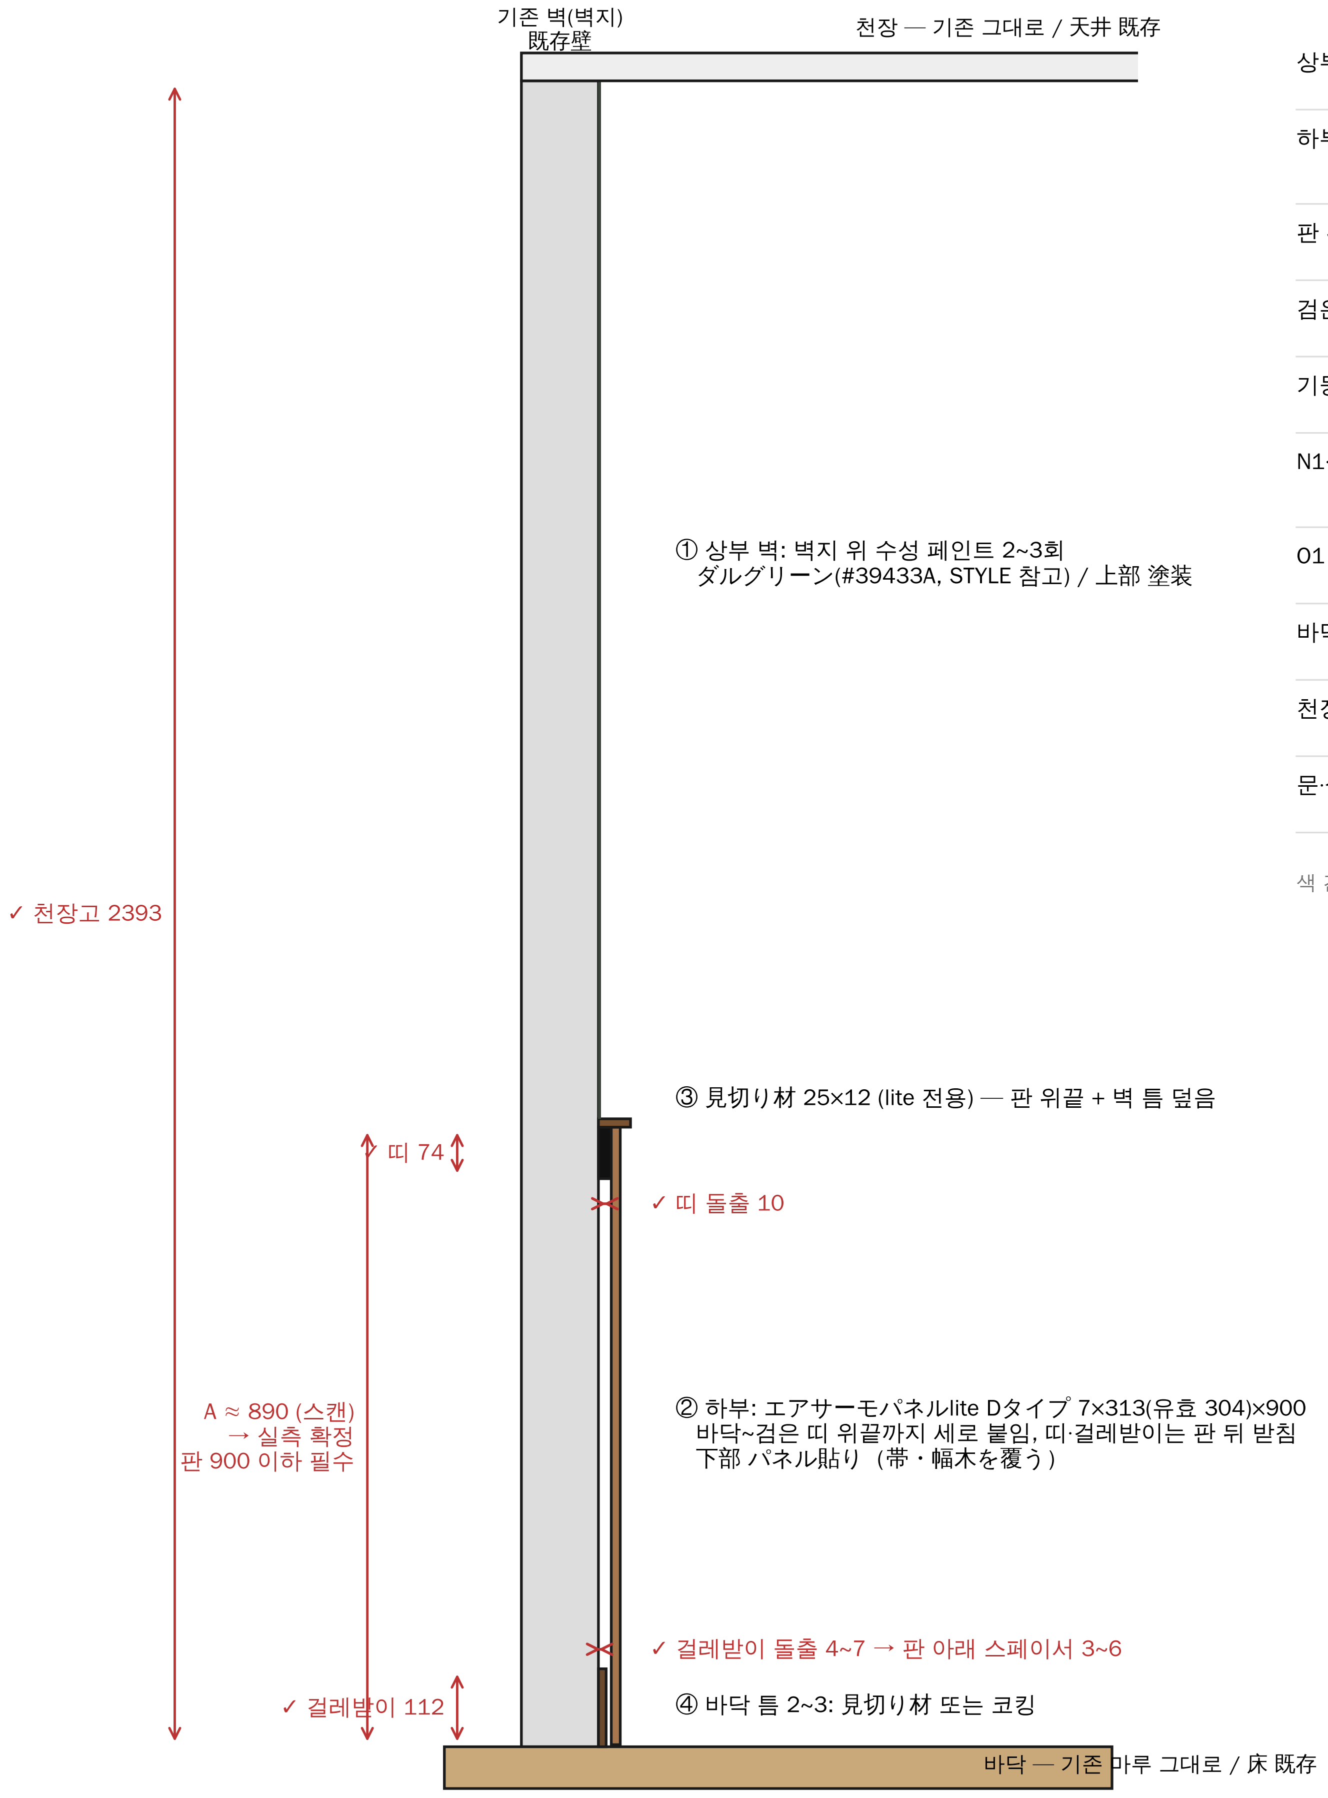
기존 벽(벽지)
既存壁
천장 — 기존 그대로 / 天井 既存
① 상부 벽: 벽지 위 수성 페인트 2~3회
ダルグリーン(#39433A, STYLE 참고) / 上部 塗装
✓ 천장고 2393
③ 見切り材 25×12 (lite 전용) — 판 위끝 + 벽 틈 덮음
띠 74
✓ 띠 돌출 10
A ≈ 890 (스캔)
→ 실측 확정
판 900 이하 필수
② 하부: エアサーモパネルlite Dタイプ 7×313(유효 304)×900
바닥~검은 띠 위끝까지 세로 붙임, 띠·걸레받이는 판 뒤 받침
下部 パネル貼り（帯・幅木を覆う）
✓ 걸레받이 돌출 4~7 → 판 아래 스페이서 3~6
✓ 걸레받이 112
④ 바닥 틈 2~3: 見切り材 또는 코킹
바닥 — 기존 마루 그대로 / 床 既存

마감 사양 / 仕上げ仕様

상부 벽 (띠 위~천장)	수성 페인트 ダルグリーン #39433A · 비닐 벽지 위 밀착 프라이머 + 2~3회. 면적 약 45~50 ㎡ (창 제외)
하부 벽 (바닥~띠 위끝)	エアサーモパネルlite D (RESTA) 7×313×900, 유효폭 304 — 약 140장(여유 포함). 양면테이프/접착: 원상복구 조건 확인
판 위끝·옆끝	lite 見切り材 25×12×1200 — 위끝 약 39 m(33본) + 옆끝(기둥 모서리·창 옆) 약 17본 → 약 50본
검은 띠·걸레받이	철거 없음. 판 뒤에 숨김
기둥 C1~C3	띠 위(≈0.89)~천장 4면 거울, 모서리 맞댐, 비산방지 필름. 아래는 판
N1·N2 신설 벽	LGS 또는 목틀 + PB 12.5 양면, 천장까지. N2 남면 크림슨 #8A1F2B 무광 페인트(띠·걸레받이 없음), 북면·N1 양면은 홀과 동일(ダルグリーン + 판)
O1 개구	W4 끝 0.53×1.98 개구, 상부 검은 봉 + 암막 커튼(짙은 회색)
바닥	기존 원목 마루 유지. F1 구간만 레드 카펫(타일 카펫 50 cm 약 18장 또는 롤)
천장·조명	기존 유지. 트랙에 스포트 3 등 추가(전구색 2700~3000K, 24~36°)
문·설비	화장실 문·세면대·싱크대 기존 유지. 콘센트가 판에 걸리면 따내기(박스 이설은 電気工事士)

색 견본: ダルグリーン은 STYLE 150 ml 견본 칠해 본 뒤 최종 결정. 판 색은 샘플로 확인 후 지정.

④ 공사 범위 · 견적 의뢰 항목 / 工事範囲・見積依頼項目

DIY 가능 항목은 표시. 업체에는 '업체' 항목 견적을 요청. 수량은 3D·실측 기준 개략 — 현장 실측 후 확정.

✓ 실측 2026-11-07 / 実測 · (스캔) = 3D 스캔 추정 / スキャン推定 — 着工前に現場再確認

No	항목 / 項目	사양 / 仕様	수량(개략)	시공	비고
1	N1 주방 입구 막음 벽	1.12 × H2.39, t0.10, 양면 PB, 홀 마감	1개소	업체	현 입구 소핏 아래
2	N2 레지 뒤 벽	2.30 × H2.39, t0.10, 남면 크림슨 페인트 / 북면 홀 마감	1개소	업체	홀 쪽 통로 0.60 확보
2b	N3·N4 사진 코너 날개벽	각 1.10 × H2.39, t0.10, 양면 홀 마감	2개소	업체	사이드보드 양옆
2c	N5 화장실 문 가림벽	1.13 × H2.39, t0.10, 문에서 0.80, 동쪽 끝 W1 에 붙임	1개소	업체	위치 현장 조정
2d	N6 아치 출입구	폭 0.86, 스프링 1.62, 꼭대기 2.05 반원 — 상부 스팬드럴 + 금색 몰딩	1개소	업체	N4~N5 사이
2e	N7 홀 입구 아치	폭 0.90, 스프링 1.62, 꼭대기 2.07 반원 — 상부 스팬드럴 + 금색 몰딩	1개소	업체	N2~N3 사이
8b	P3 화장실 앞 포토 스폿	거울 벽(N5 안쪽 면 1.13×2.39 ≈ 2.7 ㎡) + 옆 아치 벽(N6) 포토 스폿 쪽 면(아치 제외 ≈ 0.4 ㎡)만 리프 모자이크 타일(≈ 3.1 [illegible]) + 금테 타원 거울 64×92. [illegible]은 무지 크림색 페인트 + 같은 크림 톤 체어레일 H0.92(45×18)·걸레받이 H0.10	1식	업체(타일) + DIY(페인트)	[illegible]
8c	D2 화장실 문 교체	폭 0.645, 경첩 동쪽, 안여닫이(세면실 쪽), 월넛(적갈색) 2단 패널 문 + 새틴 니켈 레버, 도어클로저	1개소	업체	기존 바깥여닫이 회색 철문 철거
D	C1·C3 철거	얇은 기둥 2본 — 구조 기둥이면 불가. 구조 확인 선행	2본	업체(구조)	계획 단계
3	O1 W4 개구 + 커튼	0.53 × H1.98 개구, 보강, 검은 봉 + 암막 커튼	1개소	업체	구조 확인
4	상부 벽 페인트	ダルグリーン, 프라이머 + 2~3회	약 45~50 ㎡	업체 또는 DIY	벽지 상태·밀착 테스트
5	하부 벽 판 + 見切り材	エアサーモパネルlite 7 mm, 바닥~띠 위끝, 見切り材 25×12	판 약 140장 · 見切り材 약 50본	DIY 예정	높이 A 실측 후 발주
6	기둥 4면 거울	C1~C3 띠 위~천장, 비산방지 필름, 모서리 맞댐	3기둥 × 4면 = 12면 (약 13 ㎡)	업체(거울점)	치수 현장 실측
7	레드 카펫	입구 통로 1.09×1.31 + 레지 앞 2.19×0.99	약 3.6 ㎡	업체 또는 DIY	타일 카펫 가능
8	간판 글씨·거울	船場美術館 세로 금박 절단문자 H1.1 · 원형 거울 φ0.55	1식	업체(사인)	N2 남면
9	조명 추가	트랙 스포트 3등 (2700~3000K)	3등	업체(전기) / DIY	기존 트랙 이용
10	레지 카운터	0.8×0.45×H1.0 (제작 또는 기성)	1대	제작 또는 구입	벽 2 에 붙임
11	콘센트·스위치	판 시공 구간 따내기, 필요 시 박스 이설	현장 확인	업체(전기)	電気工事士
—	기존 유지	바닥 마루 · 천장 · 검은 띠 · 걸레받이 · 창 · 화장실 문 · 싱크대 · 자동문			철거 없음

업체 확인 요청 / 業者への確認事項

- 임대 원상복구(原状回復) 조건에 맞는 고정 방식(신설 벽 바닥·천장 고정, 판 접착) 제안
- N1·N2 가 천장 트랙·에어컨·스프링클러·배선과 간섭하는지
- 벽지 위 페인트 가능 여부(비닐/오염방지 코팅), 필요 시 프라이머 종류
- 기둥 거울 시공 방식(접착 + 비산방지 필름, 모서리 처리)과 안전 기준
- 공사 기간 및 영업 중 시공 가능 여부
- 견적은 항목별(1~11) 분리 — DIY 항목은 자재만 또는 제외

첨부: 3D 뷰어(E안) https://85mighty.github.io/senba-ops/kobe-interior/kobe-gallery-3d/app/ · 현장 사진 11장 · 실측 손글씨 평면도(11/07)